


MECHANICAL WORKING DRAWINGS

List of Drowing

Sheet Name	Sheet Number
Series-0000 General	
cover 1	MH-0000
list of drowing	MH-0001
1 - HVAC	
Series-0000 General	
HVAC 3D VIEW	MH-0002
EQUIPMENT SCHEDULE	MH-0003
Series-1000 Duct Work	
GROUND FLOOR PLAN	MH-1100
FIRST F.P - HVAC SYSTEM LAYOUT	MH-1200
Roof Floor Plan	MH-1300
Series-4000 Details	
Details	MH-4001
Details	MH-4002
2 - DOMESTIC	
Series-0000 General	
Plumbing Cover	PP-0000
Plumbing 3D View	PP-0001
Series-1000 DOMESTIC Work	
G. F. P - WATER SUPPLY	PP-1100
F. F. P - WATER SUPPLY	PP-1200
R. F. P - WATER SUPPLY	PP-1300
Series-1800 Details	
ENLARGED DETAILS	PP-1801
3D-ENLARGED DETAILS	PP-1802
3D-ENLARGED DETAILS	PP-1803
3D-ENLARGED DETAILS	PP-1804
DETAILS	PP-1805
DETAILS	PP-1806
3 - DRAINAGE	
Series-0000 General	
Plumbing 3D View	PY-0001
Series-1000 DRAINAGE Work	
G.F.P - DRAINAGE SYSTEM LAYOUT	PY-1100
F.F.P - DRAINAGE SYSTEM LAYOUT	PY-1200
R.F.P - DRAINAGE SYSTEM LAYOUT	PY-1300
Series-2000 CONDENSATE DRAIN	
G.F.P - CONDENSATE SYSTEM LAYOUT	PY-2100
F.F.P - CONDENSATE SYSTEM LAYOUT	PY-2200
Series-9000 Details	
Enlarged Details	PY-9001
3D Enlarged Details	PY-9002
DETAILS	PY-9003
DETAILS	PY-9004

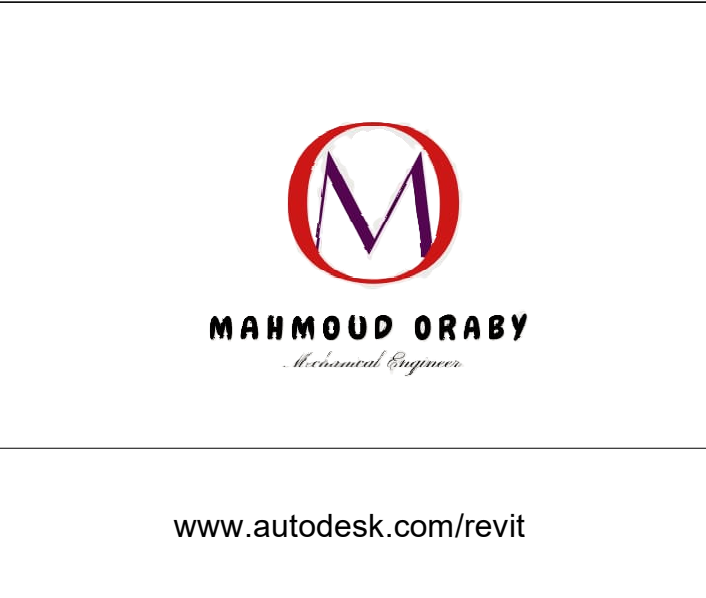

Consultant	Consultant
Address	Address
Address	Address
Phone	Phone
Fax	Fax
e-mail	e-mail
Consultant	Consultant
Address	Address
Address	Address
Phone	Phone
Fax	Fax
e-mail	e-mail

[illegible]

Owner	
Villa Badria	
list of drowing	
Project number	Project Number
Date	Issue Date
Drawn by	Author
Checked by	Checker
MH-0001	
Scale	



www.autodesk.com/revit

Consultant
Address
Address
Phone
Fax
e-mail

Consultant
Address
Address
Phone
Fax
e-mail

Consultant
Address
Address
Phone
Fax
e-mail

Consultant
Address
Address
Phone
Fax
e-mail

Mechanical Equipment Schedule				
EQUIPMENT	Type	COOLING LOAD	Level	Count
GROUND FLOOR PLAN -				
FCU	282 LPS	18000 Btu/h	GROUND FLOOR PLAN -	1
FCU	188 LPS	24000 Btu/h	GROUND FLOOR PLAN -	1
FCU	188 LPS	24000 Btu/h	GROUND FLOOR PLAN -	1
FCU	188 LPS	24000 Btu/h	GROUND FLOOR PLAN -	1
FCU	282 LPS	18000 Btu/h	GROUND FLOOR PLAN -	1
SPLIT .INDOOR UNIT WALL	Split AC 1 TR (FCU)	12000 Btu/h	GROUND FLOOR PLAN -	1
SPLIT .INDOOR UNIT WALL	Split AC 1 TR (FCU)	12000 Btu/h	GROUND FLOOR PLAN -	1
FRESH FAN	BDTX 100		GROUND FLOOR PLAN -	1
EXHOUST FAN	BDTX 100		GROUND FLOOR PLAN -	1
EXHOUST FAN	BDTX 100		GROUND FLOOR PLAN -	1
EXHOUST FAN	BDTX 100		GROUND FLOOR PLAN -	1
FIRST FLOOR PLAN -				
FCU	283 LPS	240000 Btu/h	FIRST FLOOR PLAN -	1
FCU	283 LPS	240000 Btu/h	FIRST FLOOR PLAN -	1
FCU	283 LPS	240000 Btu/h	FIRST FLOOR PLAN -	1
FCU	282 LPS	18000 Btu/h	FIRST FLOOR PLAN -	1
FCU	282 LPS	18000 Btu/h	FIRST FLOOR PLAN -	1
EXHOUST FAN	BDTX 100		FIRST FLOOR PLAN -	1
EXHOUST FAN	BDTX 100		FIRST FLOOR PLAN -	1
EXHOUST FAN	BDTX 100		FIRST FLOOR PLAN -	1
EXHOUST FAN	BDTX 100		FIRST FLOOR PLAN -	1
SECOND ROOF S.S.L.				
O.D.U	RAV-SP240AT2-UL	24000 Btu/h	SECOND ROOF S.S.L.	1
O.D.U	RAV-SP240AT2-UL	24000 Btu/h	SECOND ROOF S.S.L.	1
O.D.U	RAV-SP240AT2-UL	24000 Btu/h	SECOND ROOF S.S.L.	1
O.D.U	RAV-SP240AT2-UL	24000 Btu/h	SECOND ROOF S.S.L.	1
O.D.U	RAV-SP240AT2-UL	24000 Btu/h	SECOND ROOF S.S.L.	1
O.D.U	RAV-SP240AT2-UL	24000 Btu/h	SECOND ROOF S.S.L.	1
O.D.U	RAV-SP240AT2-UL	24000 Btu/h	SECOND ROOF S.S.L.	1
O.D.U	RAV-SP240AT2-UL	24000 Btu/h	SECOND ROOF S.S.L.	1
O.D.U	RAV-SP240AT2-UL	24000 Btu/h	SECOND ROOF S.S.L.	1
O.D.U	RAV-SP240AT2-UL	24000 Btu/h	SECOND ROOF S.S.L.	1
O.D.U	RAV-SP240AT2-UL	24000 Btu/h	SECOND ROOF S.S.L.	1
O.D.U	RAV-SP240AT2-UL	24000 Btu/h	SECOND ROOF S.S.L.	1
O.D.U	RAV-SP240AT2-UL	24000 Btu/h	SECOND ROOF S.S.L.	1
O.D.U	RAV-SP240AT2-UL	24000 Btu/h	SECOND ROOF S.S.L.	1
WATER TANK	3000X1200 (115 GALLONS)		SECOND ROOF S.S.L.	1
WATER HEATER	A13810		SECOND ROOF S.S.L.	1
PUMP	Circulation Pump		SECOND ROOF S.S.L.	1
PUMP	Circulation Pump		SECOND ROOF S.S.L.	1
PUMP	Circulation Pump		SECOND ROOF S.S.L.	1
Grand total: 37				

[illegible]

Owner

Villa Badria

EQUIPMENT SCHEDULE

Project number Project Number

Date Issue Date

Drawn by **Mahmoud Hamdy**

Checked by A.SH

HM-0003

Scale



www.autodesk.com/revit

Consultant
Address
Address
Phone
Fax
e-mail


Consultant
Address
Address
Phone
Fax
e-mail

Consultant
Address
Address
Phone
Fax
e-mail

Consultant
Address
Address
Phone
Fax
e-mail

Owner	
Villa Badria	
GROUND FLOOR PLAN	
Project number	Project Number
Date	Issue Date
Drawn by	Author
Checked by	Checker
MH-1100	
Scale	1 : 10

9/22/2024 10:12:39 PM

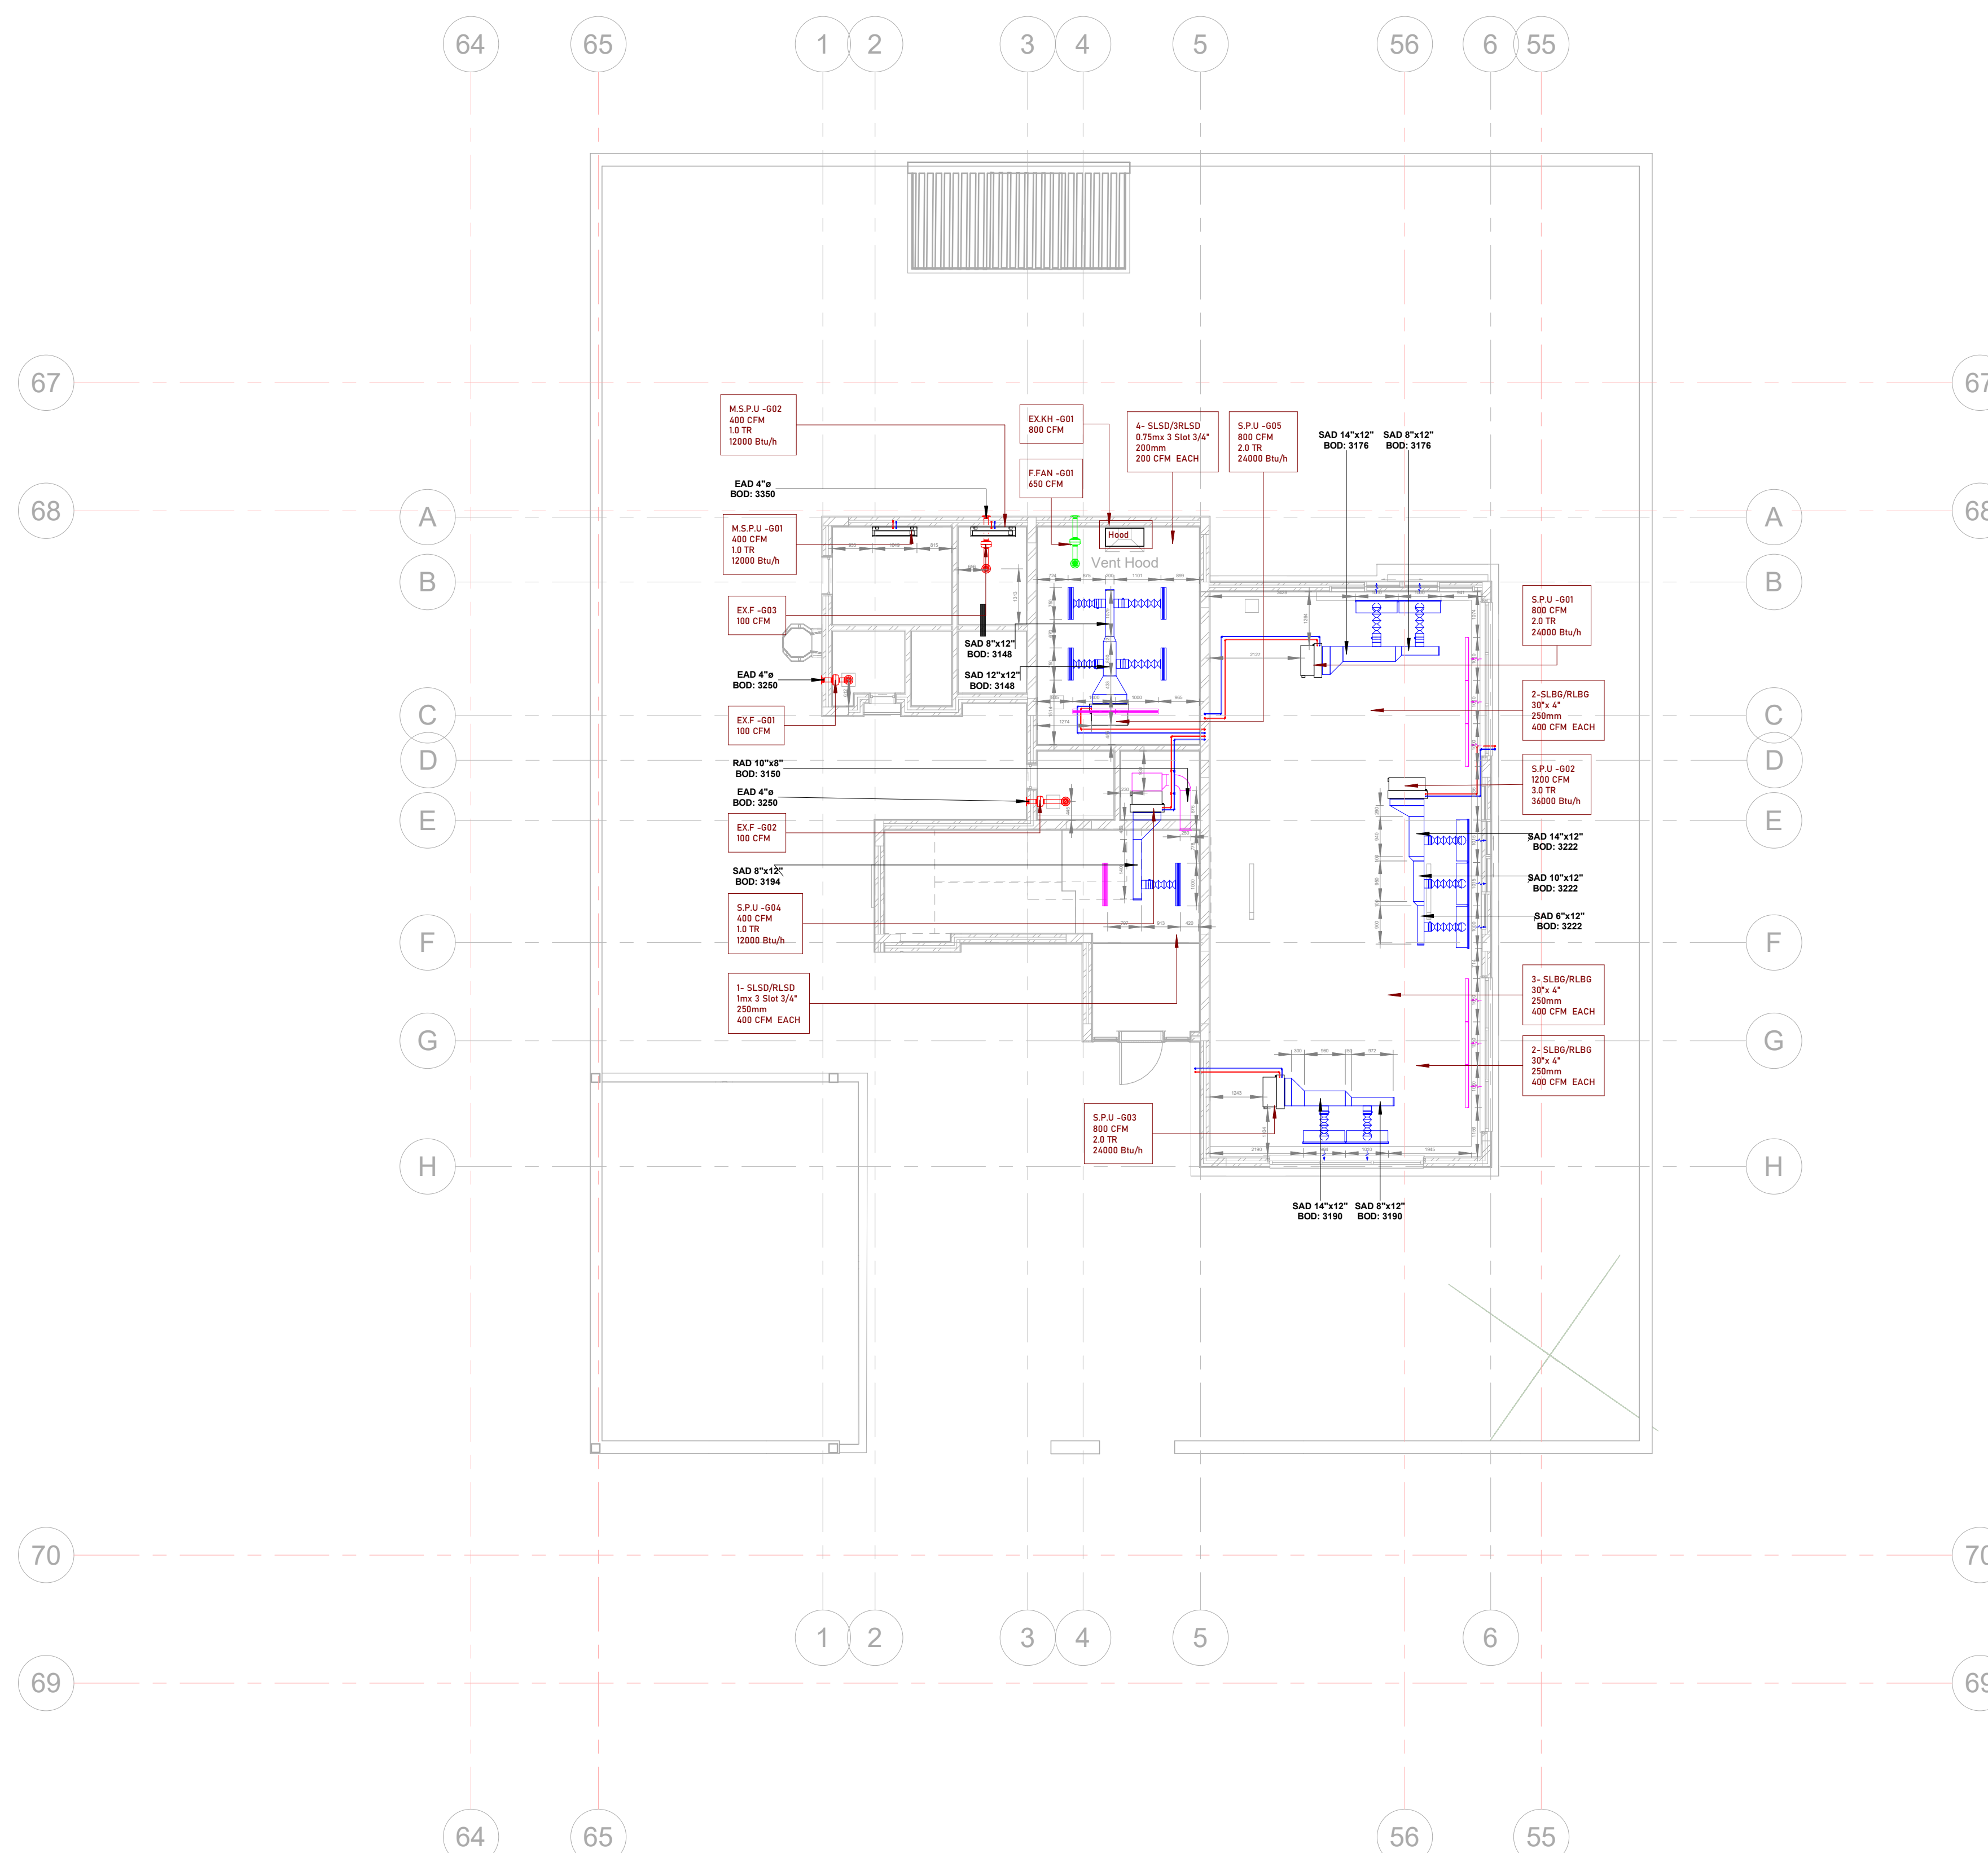

1 GROUND FLOOR PLAN -
1 : 100



www.autodesk.com/revit

Consultant
Address
Address
Phone
Fax
e-mail

Consultant
Address
Address
Phone
Fax
e-mail

Consultant
Address
Address
Phone
Fax
e-mail

Consultant
Address
Address
Phone
Fax
e-mail

Owner
Villa Badria

Project number	Project Number
----------------	----------------

Date	Issue Date
------	------------

Drawn by **Mahmoud Hamd**

Checked by	A.S
------------	-----

MH-1200

Scale	1 : 10
-------	--------







Consultant
Address
Address
Phone
Fax
e-mail

[illegible]

Owner
Villa Badria

Details

Project number	Project Number
----------------	----------------

Date	Issue Date
------	------------

Drawn by	Mahmoud Hamdy
----------	---------------

Checked by	A.SH
------------	------

MH-4002

Scale	As indicated
-------	--------------