



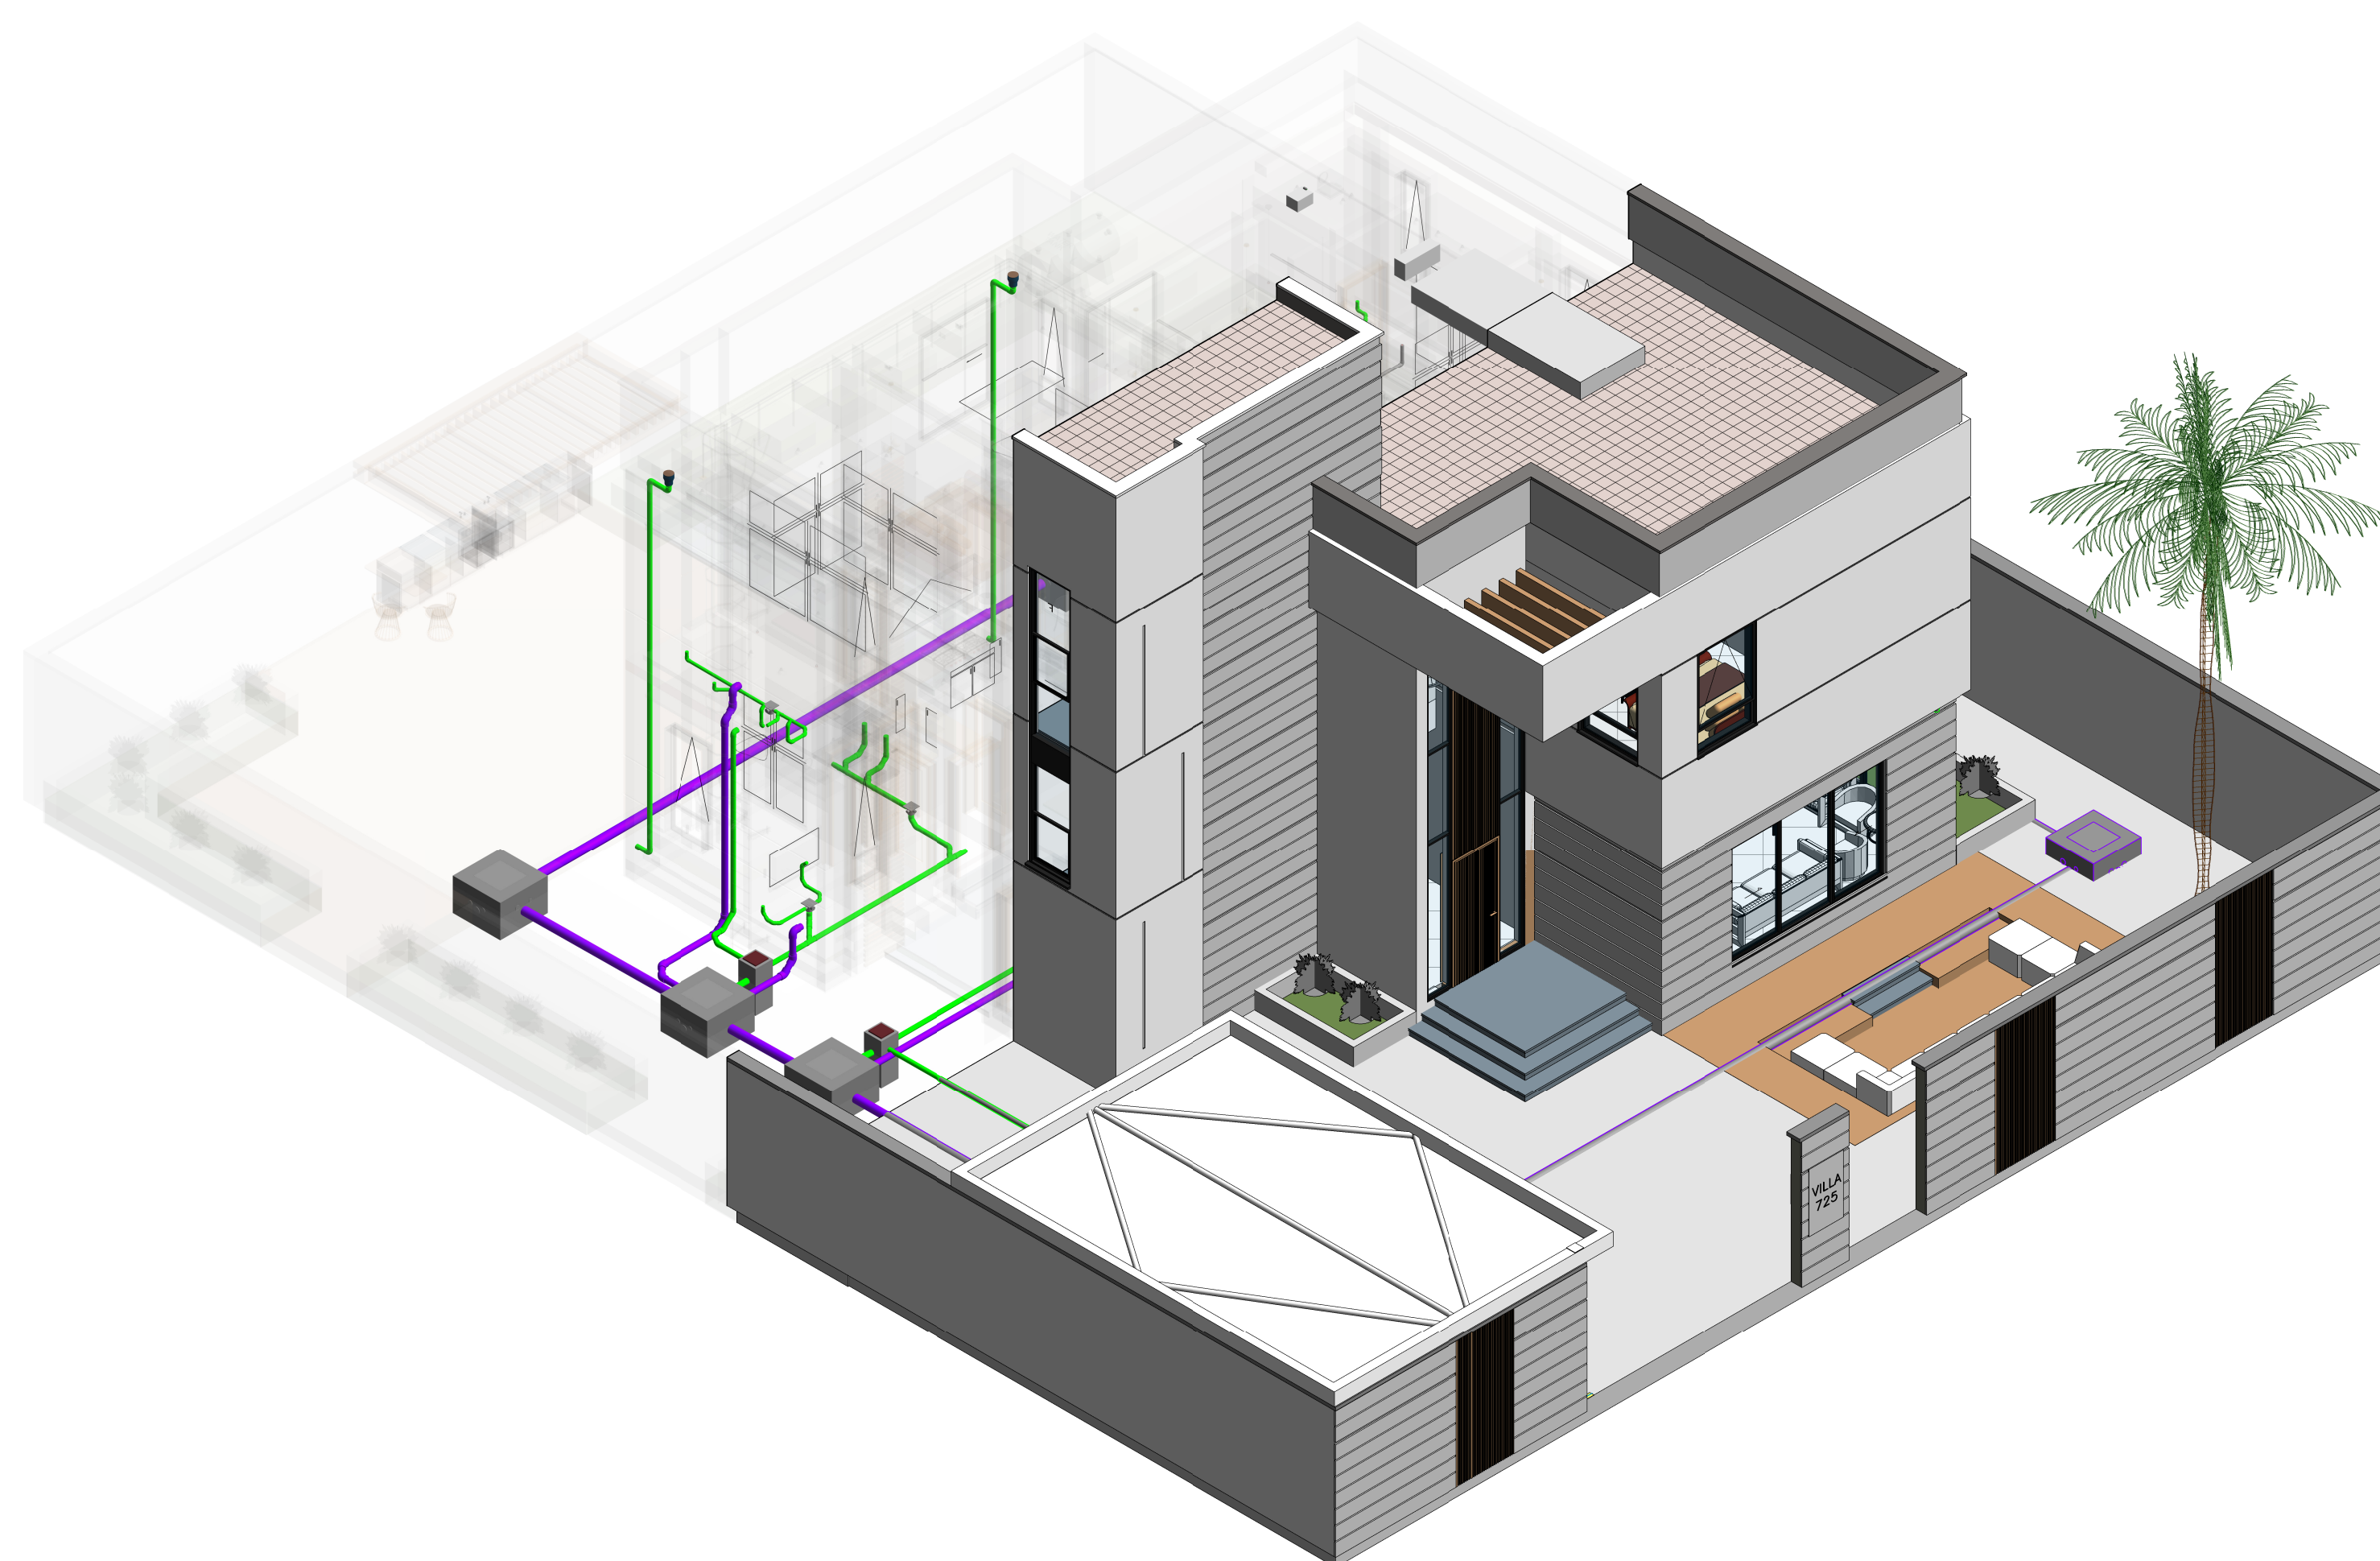
www.autodesk.com/revit

Consultant
Address
Address
Phone
Fax
e-mail

Consultant
Address
Address
Phone
Fax
e-mail

Consultant
Address
Address
Phone
Fax
e-mail

Consultant
Address
Address
Phone
Fax
e-mail

[illegible]

Owner

Villa Badria

Plumbing 3D View

Project number	Project Number
----------------	----------------

Date	Issue Date
------	------------

Drawn by	Author
----------	--------

Checked by	Checker
------------	---------

PY-0001

Scale



Consultant
Address
Address
Phone
Fax
e-mail

Consultant
Address
Address
Phone
Fax
e-mail

Consultant
Address
Address
Phone
Fax
e-mail

Consultant
Address
Address
Phone
Fax
e-mail

[illegible]

Owner

Villa Badria

F.F.P - DRAINAGE SYSTEM LAYOUT

Project number	Project Number
----------------	----------------

Date	Issue Date
------	------------

Drawn by	Mahmoud Hamdy
----------	---------------

Checked by	A.SH
------------	------

PY-1200

Scale	1 : 100
-------	---------





Consultant
Address
Address
Phone
Fax
e-mail

Consultant
Address
Address
Phone
Fax
e-mail

Consultant
Address
Address
Phone
Fax
e-mail

Consultant
Address
Address
Phone
Fax
e-mail

[illegible]

Owner

Villa Badria

F.F.P - CONDENSATE SYSTEM LAYOUT

Project number	Project Number
----------------	----------------

Date	Issue Date
------	------------

Drawn by	Author
----------	--------

Checked by	Checker
------------	---------

PY-2200

Scale	1 : 100
-------	---------

